

SƠ ĐỒ MỘT SỢI TBA XUÂN ĐÌNH 17

SCHNEIDER - RM6

Tủ RMU 24KV - 630A

Cáp 24kV - 3x240mm²

Điểm đầu đầu búc vào tuyến CN
từ XD 2 đi TT HC- lộ 475E21

Cáp 24KV - 3(1x50)mm²
(Cáp sang MBA)

MBA: 1000kVA - 22/0,4kV

Tổ đấu dây: D/Yo-11

12 sợi Cáp 0,6/1kV Cu/XLPE/PVC - 1x240mm²
Mỗi pha 3 sợi

Tủ hạ thế 600V-1600A.

- 6 TI:1600/5A

- Aptomat tổng:

+ A1 - 1600A(ABB)

- Thanh cái MT - 2x100x5.

- Aptomat nhánh:

+ A1.1: 400A(ABB)

+ A1.2: 400A(ABB)

+ A1.3: 400A (ABB)


+ A1.4: 400A (ABB)

+ A1.5: 400A (ABB)

+ A1.6: 400A (ABB)

+ A1.7: 160A (ABB)

- Chống sét van hạ thế GZ-500V

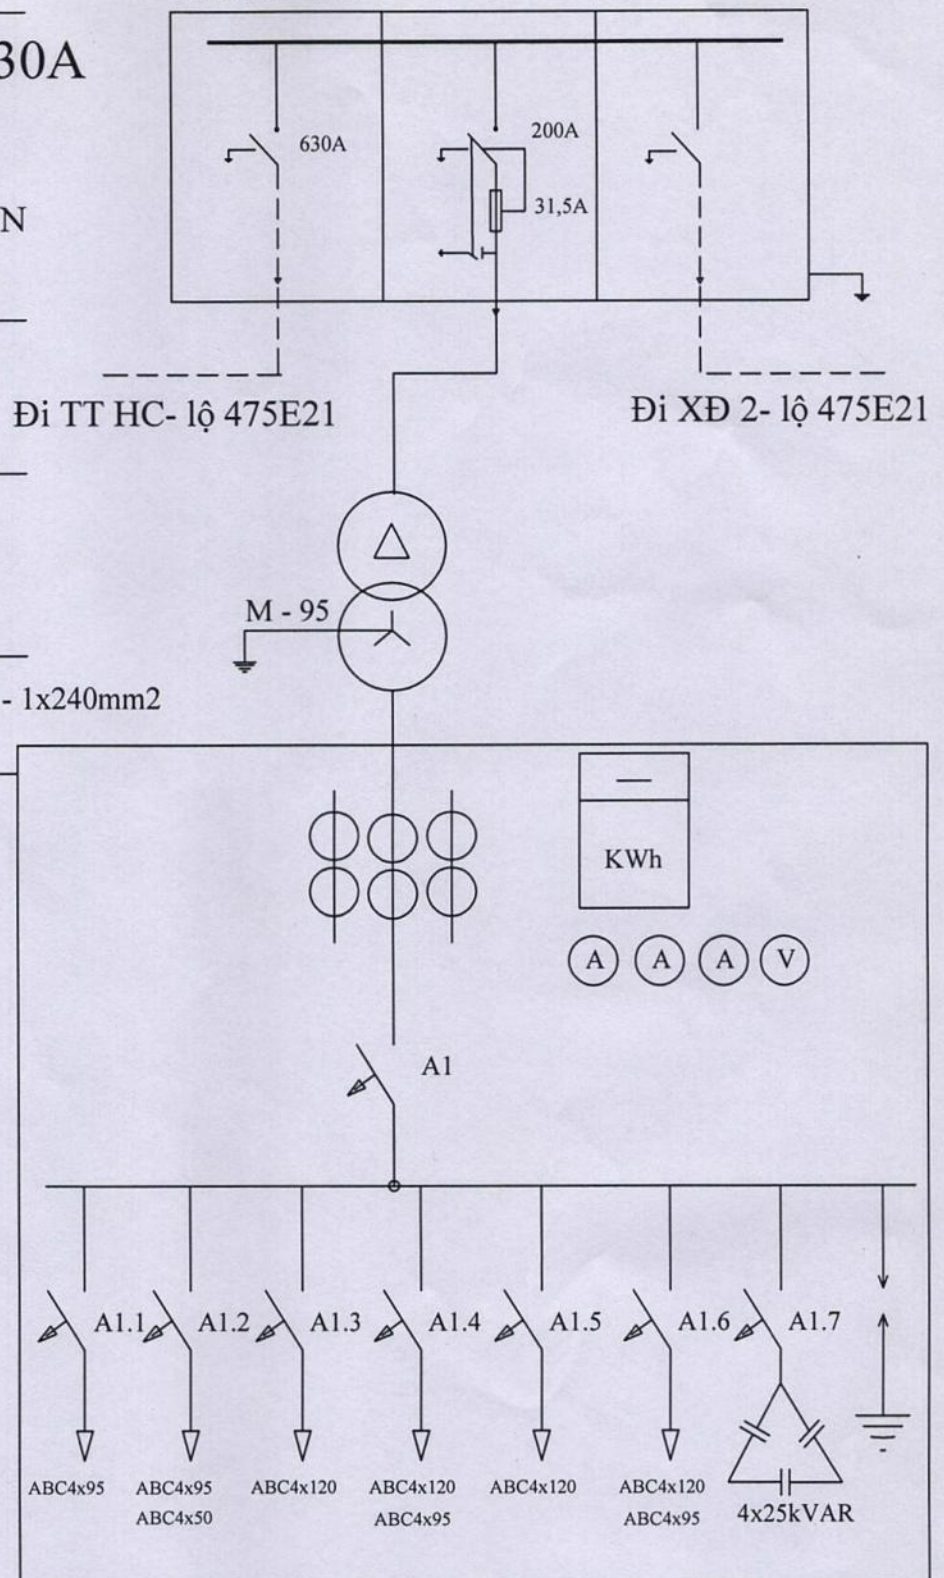

TỔNG CÔNG TY ĐIỆN LỰC HÀ NỘI
CÔNG TY ĐIỆN LỰC BẮC TỰ LIÊM

TBA XUÂN ĐÌNH 17
1000KVA - 22/0,4KV

Phó Giám Đốc

PHẠM DUY HUÂN

P Kỹ thuật AT

NGUYỄN NAM THANH

Khảo sát và vẽ

LÊ THỊ HẢI

SƠ ĐỒ MỘT SỢI

Hà Nội 10-2017

Tỷ lệ:

BV01